


Lageplan Schlossstufen

Maßstab 1:150

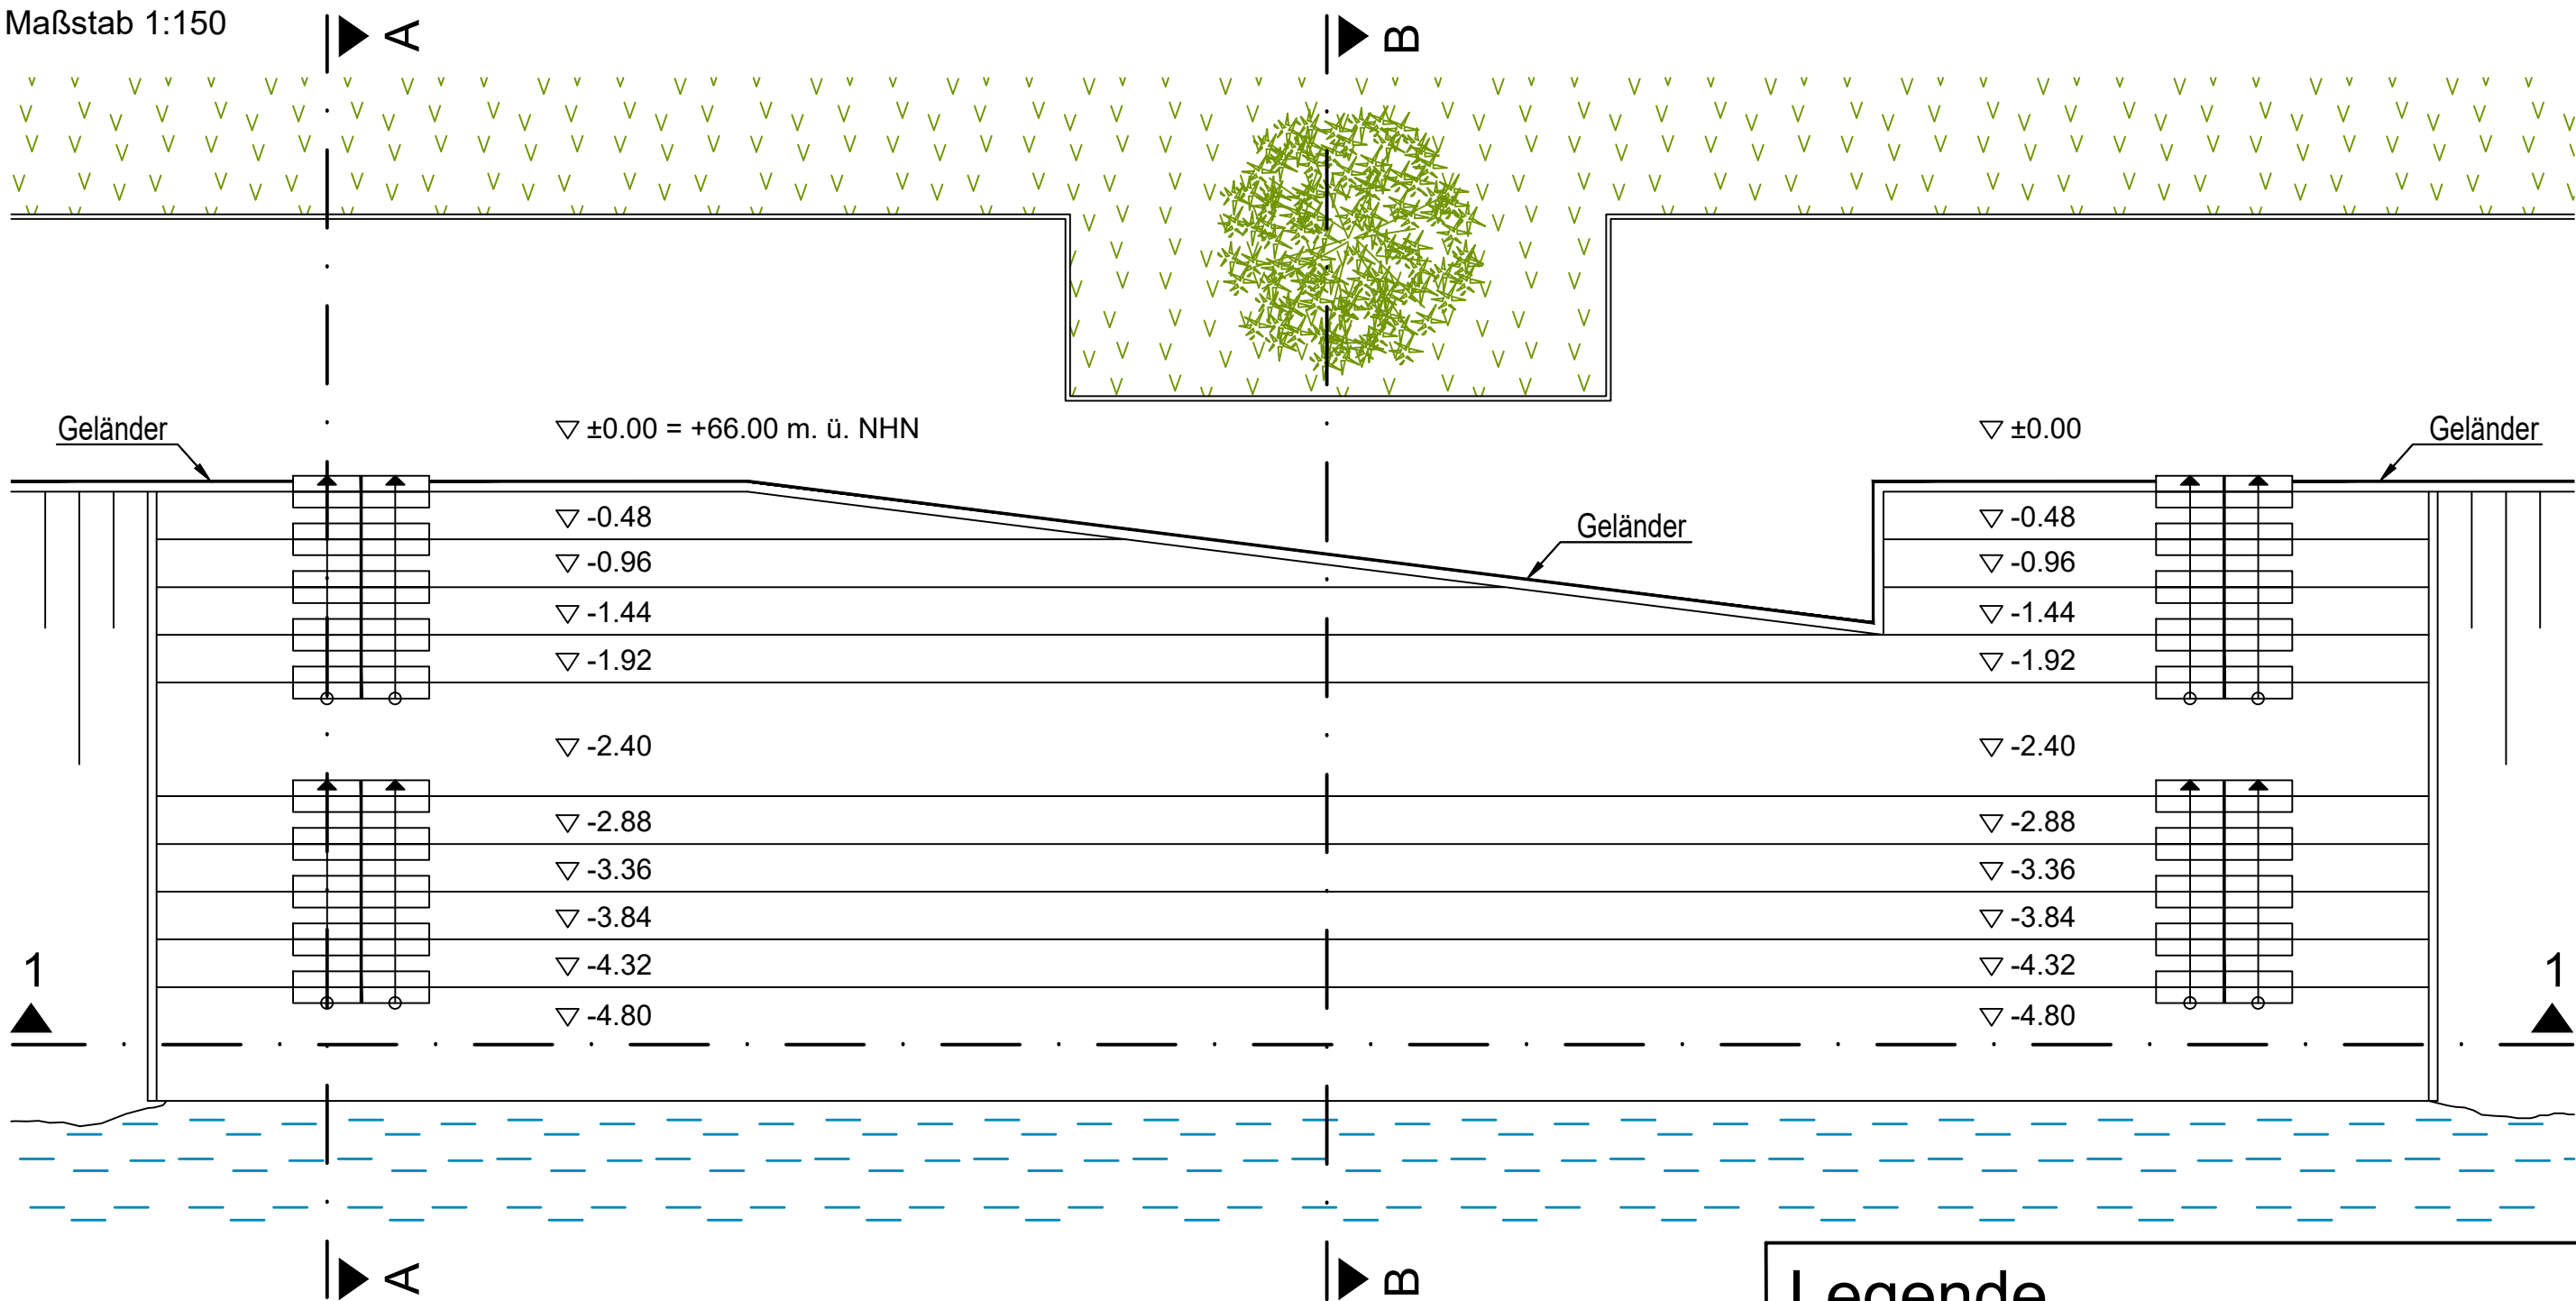

Legende

- | | |
|-----------------------|------------------|
| Stahlbeton C30/37 XF4 | Splitbettung 1/3 |
| Magerbeton C16/20 X0 | Schotter 0/45 |
| Erdreich | Gewässer (Rhein) |

Alle Sitzflächen mit 2% Gefälle Richtung Rhein

Alle Höhen beziehen sich auf +66.00 m. ü. NHN

CBS Carl Benz Schule - Lernfeld Treppe

Maßstab:

1:150

Maßeinheit:

m,cm

Modell Schlossstufen

Entwurfszeichnung - Seite 9
Lageplan

Datum:

09.06.2026

Namen:


Phee, Paul,
Stefan, Joel

Bodenaufbau 1
Pflasterstein, d = 12cm
Splittbettung, d = 4cm
Schottertragschicht, min. d = 30cm

Bodenaufbau 2
Mutterboden, d = 20cm
Schottertragschicht, min. d = 30cm

Schnitt 1-1

Maßstab 1:150

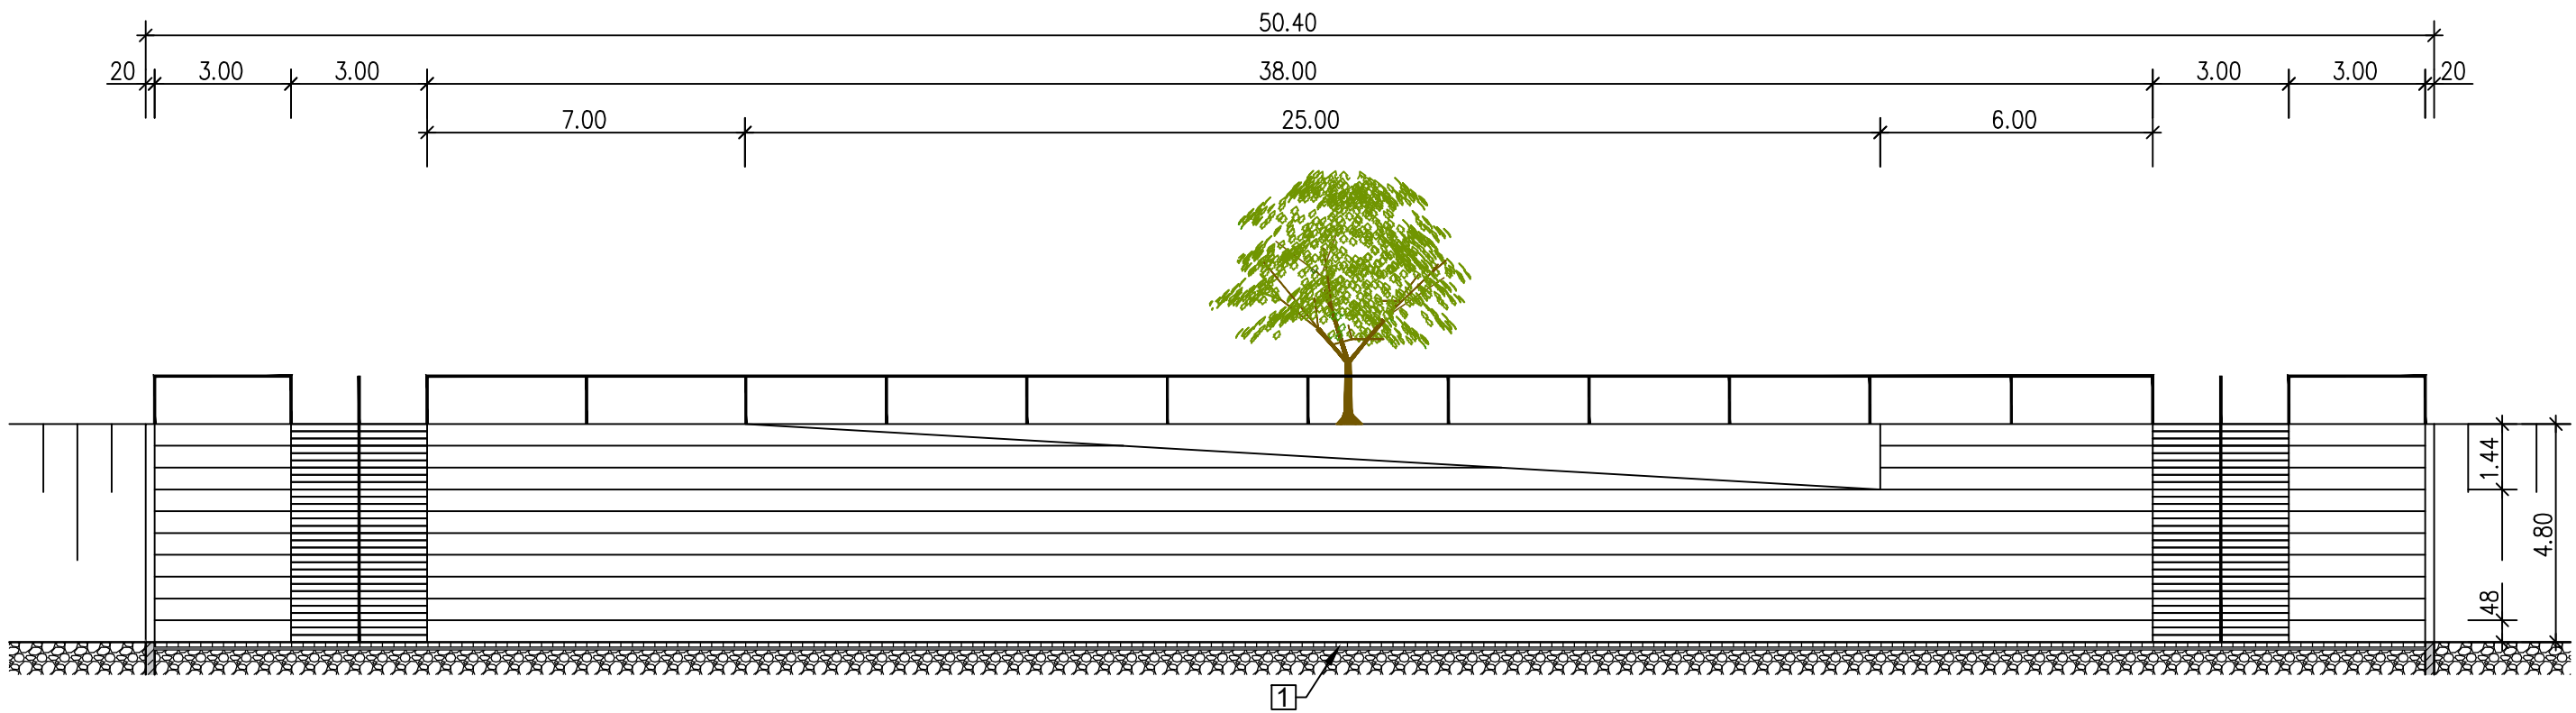

Legende


- | | |
|-----------------------|-------------------|
| Stahlbeton C30/37 XF4 | Splittbettung 1/3 |
| Magerbeton C16/20 X0 | Schotter 0/45 |
| Erdreich | Gewässer (Rhein) |
- Alle Sitzflächen mit 2% Gefälle Richtung Rhein
Alle Höhen beziehen sich auf +66.00 m. ü. NHN

CBS Carl Benz Schule - Lernfeld Treppe

Maßstab: 1:150,25	Modell Schlossstufen	Datum: 09.06.2026
Maßeinheit: m,cm		Namen: Phee, Paul, Stefan, Joel
Entwurfszeichnung - Seite 10 Draufsicht Lageplan		

Schnitt B-B

Maßstab 1:100

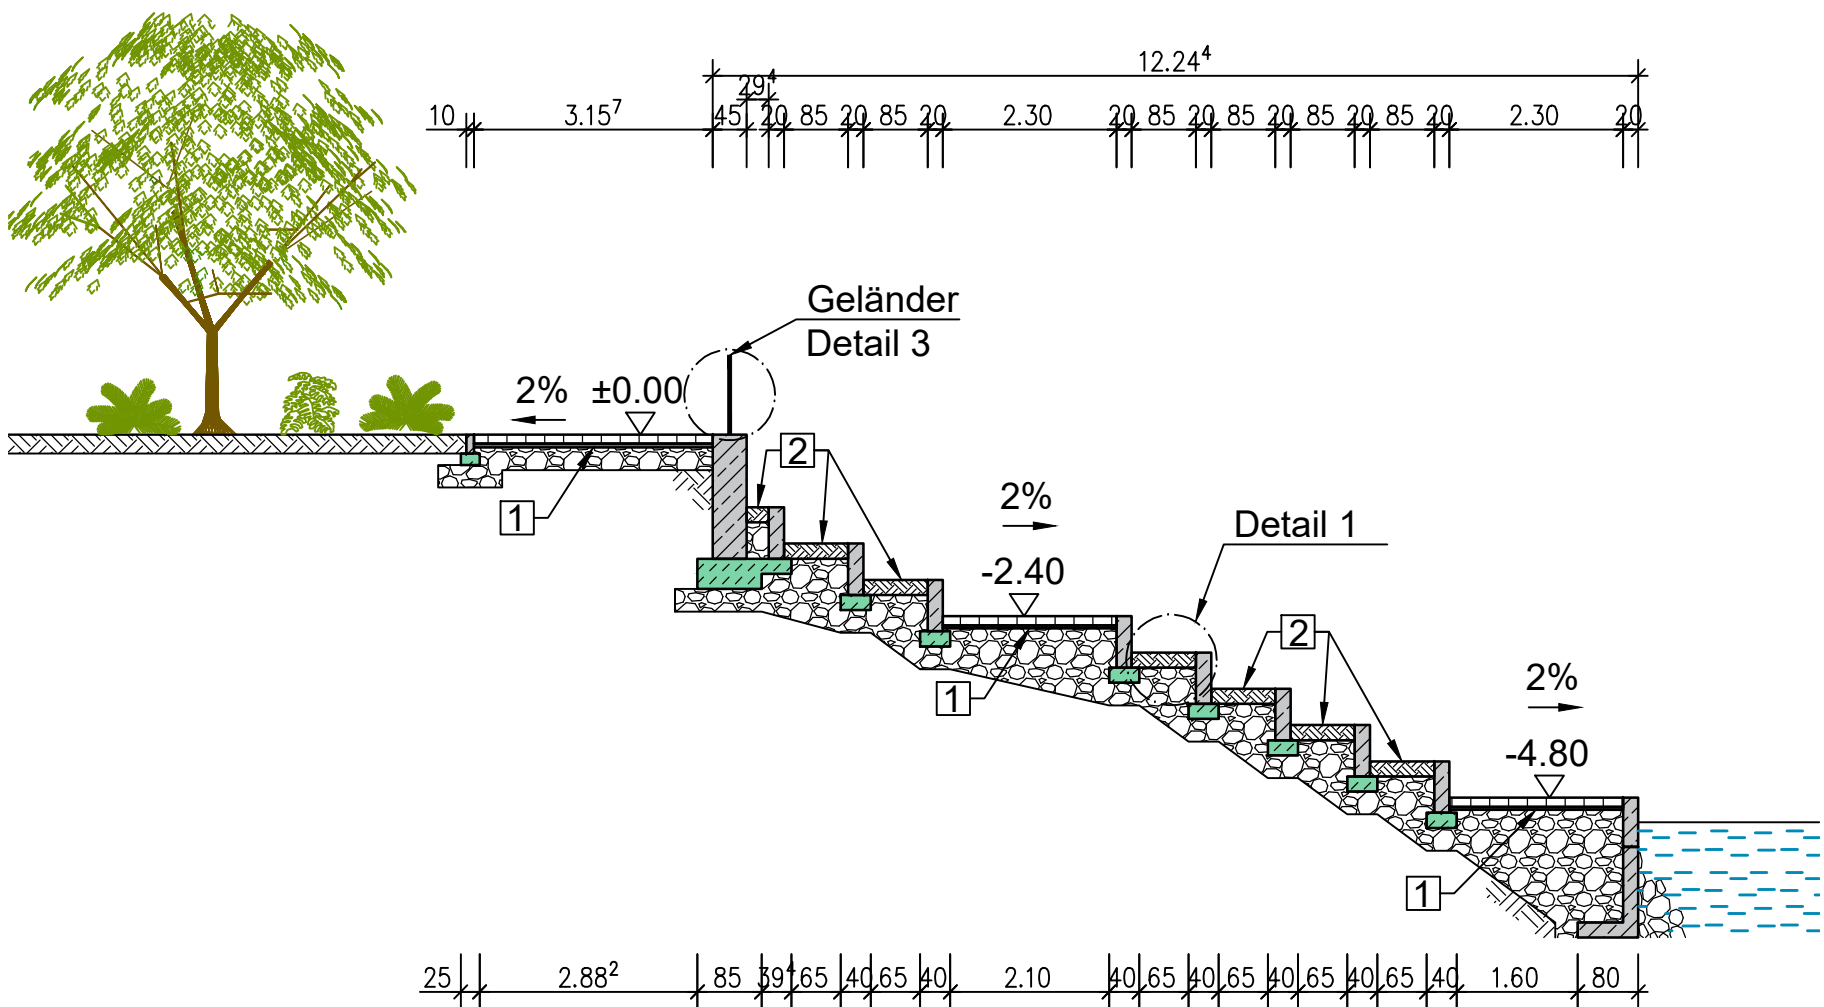

- Bodenaufbau 1**
Pflasterstein, d = 12cm
Splittbettung, d = 4cm
Schottertragschicht, min. d = 30cm
- Bodenaufbau 2**
Mutterboden, d = 20cm
Schottertragschicht, min. d = 30cm

Legende


- | | | | |
|--|-----------------------|--|-------------------|
| | Stahlbeton C30/37 XF4 | | Splittbettung 1/3 |
| | Magerbeton C16/20 X0 | | Schotter 0/45 |
| | Erdreich | | Gewässer (Rhein) |
- Alle Sitzflächen mit 2% Gefälle Richtung Rhein
Alle Höhen beziehen sich auf +66.00 m. ü. NHN

CBS Carl Benz Schule - Lernfeld Treppe

<u>Maßstab:</u>	Modell Schlossstufen	<u>Datum:</u>
1:100		09.06.2026
<u>Maßeinheit:</u>		<u>Namen:</u>
m,cm	Entwurfszeichnung - Seite 12 Schnitt A-A, Schnitt B-B	Phee, Paul, Stefan, Joel


Detail 1 - Isometrie Sitzstufe

Maßstab 1:25

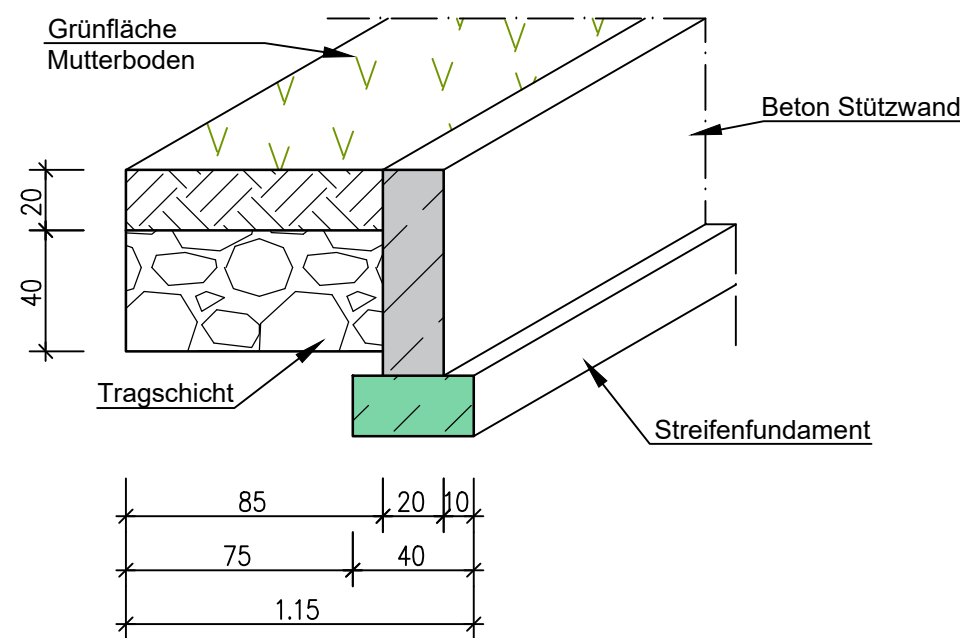


Detail 2 - Isometrie Treppenstufe

Maßstab 1:25

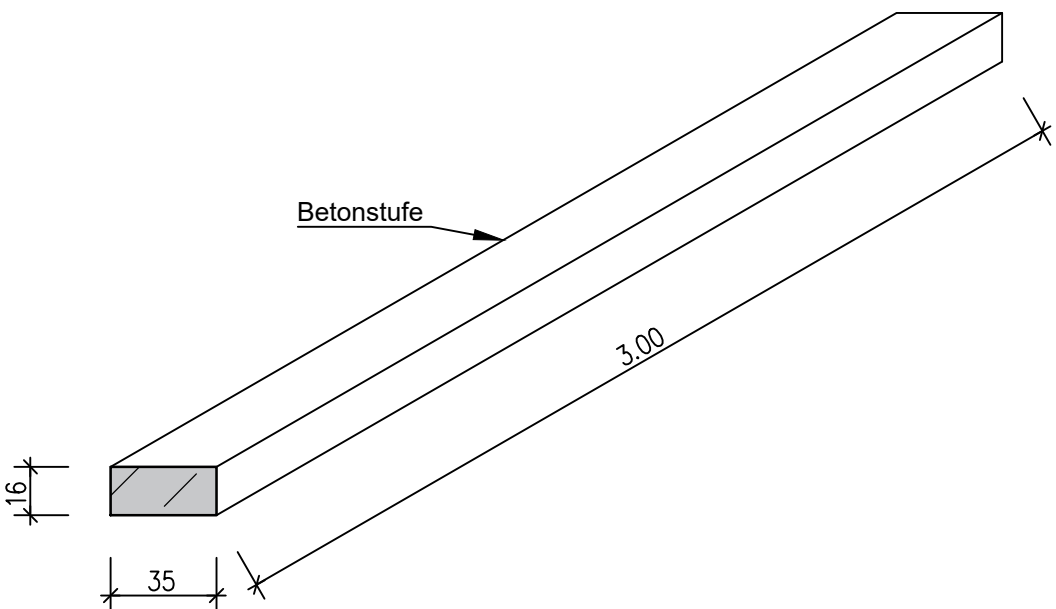

Detail 3 - Isometrie Geländer

Maßstab 1:25

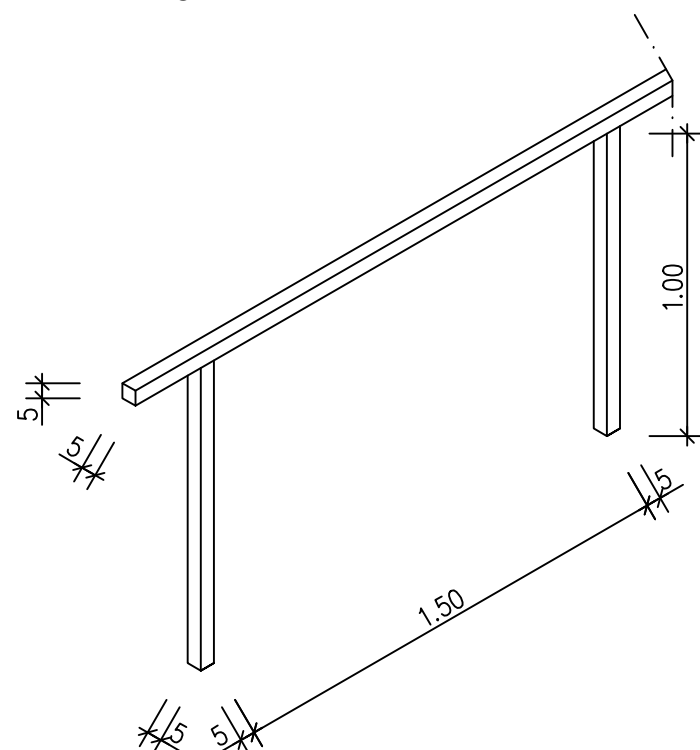

Legende

- | | |
|-----------------------|------------------|
| Stahlbeton C30/37 XF4 | Splitbettung 1/3 |
| Magerbeton C16/20 X0 | Schotter 0/45 |
| Erdreich | Gewässer (Rhein) |
- Alle Sitzflächen mit 2% Gefälle Richtung Rhein
Alle Höhen beziehen sich auf +66.00 m. ü. NHN

CBS Carl Benz Schule - Lernfeld Treppe

<u>Maßstab:</u> 1:25	Modell Schlossstufen	<u>Datum:</u> 09.06.2026
<u>Maßeinheit:</u> m,cm		<u>Namen:</u> Phee, Paul, Stefan, Joel
Entwurfszeichnung - Seite 13 Details 1-3		